



|                                     |                               |
|-------------------------------------|-------------------------------|
| <input type="checkbox"/>            | Buy America Compliant         |
| <input type="checkbox"/>            | For NYCT/MTA Review & Comment |
| <input type="checkbox"/>            | For NYCT/MTA Approval         |
| <input checked="" type="checkbox"/> | For Designer Approval         |
| <input type="checkbox"/>            | For NYCT/MTA Information Only |
| <input type="checkbox"/>            | For Designer Information Only |

Date: 10/23/2025

Contract Number: A37806 Contract Title: Design-Build Services for Accessibility Upgrades - Package 6

Item Description: Rubbing Board for Burnside Ave and Middletown Road

Submittal No.: A37806\_06 60 00\_GEN-001 Rev.: 0

Spec./ PRDC Ref.: 06 60 00 Edge Strip Rubbing Board

Location (where used): Burnside Ave Station and Middletown Road Station (A Division)

Drawing No.: NA


MLJTC2 PM's Review: Ravi Jain

MLJTC2 Quality Manager: Nabeel Anjum

Number of Pages 5  
(Including Cover Sheet):

Notes: This submittal has been reviewed by the Project Manager and  
Quality Manager to certify that it meets the contract requirements.



|  |
|--|
|  |
|  |
|  |

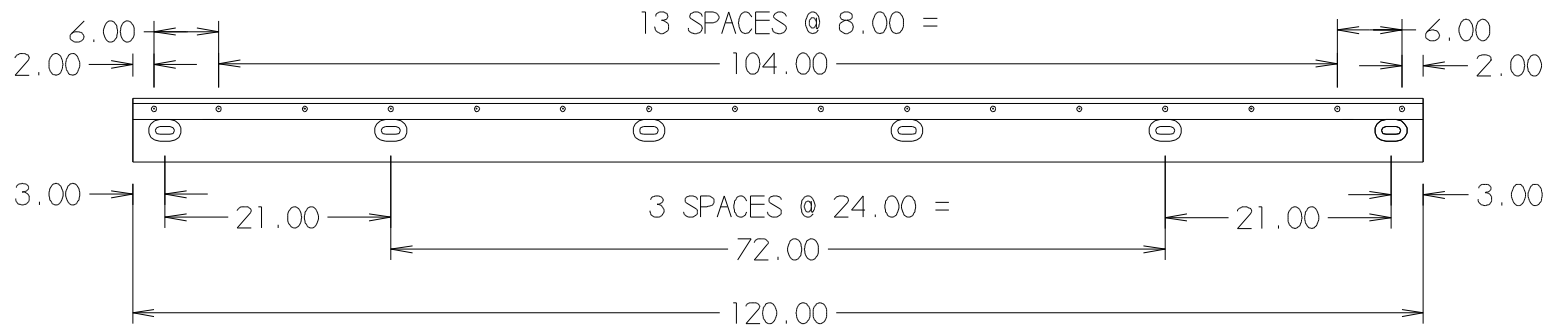

FOR 4.50 X 6 2-PC PROFILE AND TOPSIDE TREATMENT DETAIL, SEE PU-250307-TS-2

ADA Boarding Areas at Middletown  
Road and Burnside Ave


|   |     |                    |                                                                                    |  |                          |
|---|-----|--------------------|------------------------------------------------------------------------------------|--|--------------------------|
| UNLESS OTHERWISE SPECIFIED<br>UNITS = INCHES   |     |                    | POLYMER INDUSTRIES - ULTRAPOLY DIVISION<br>2404 CENTER STREET - TACOMA, WA - 98409 |  |                          |
| X.X   | +/- | .125               | TITLE<br><br>3.5 AND 4.5 X 6 X 120 2-PC 3IN ES ELV                                 |  |                          |
| X.XX   | +/- | .063               |                                                                                    |  |                          |
| X.XXX   | +/- | .032               |                                                                                    |  |                          |
| ANGLES   | +/- | 1.0°               |                                                                                    |  |                          |
| DRAWN BY<br>BDO   |     | DATE<br>03/07/2025 | REF<br>-                                                                           |  | REV<br>-                 |
| CHECKED BY<br>BDO   |     | DATE<br>03/07/2025 | MATERIAL<br>AR819FR YELLOW                                                         |  | DWG NO<br>PU-250307-TS-1 |
| POLYMER INDUSTRIES PROPRIETARY. CONFIDENTIAL. AND/OR TRADE SECRET<br>DO NOT USE, REPRODUCE, PUBLISH OR DISCLOSE TO OTHERS WITHOUT EXPRESS WRITTEN AUTHORIZATION BY POLYMER INC. |     |                    |                                                                                    |  |                          |

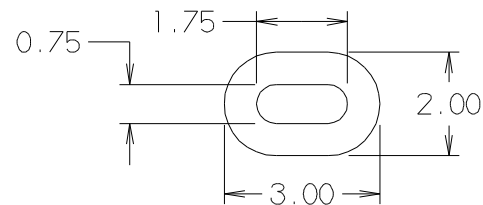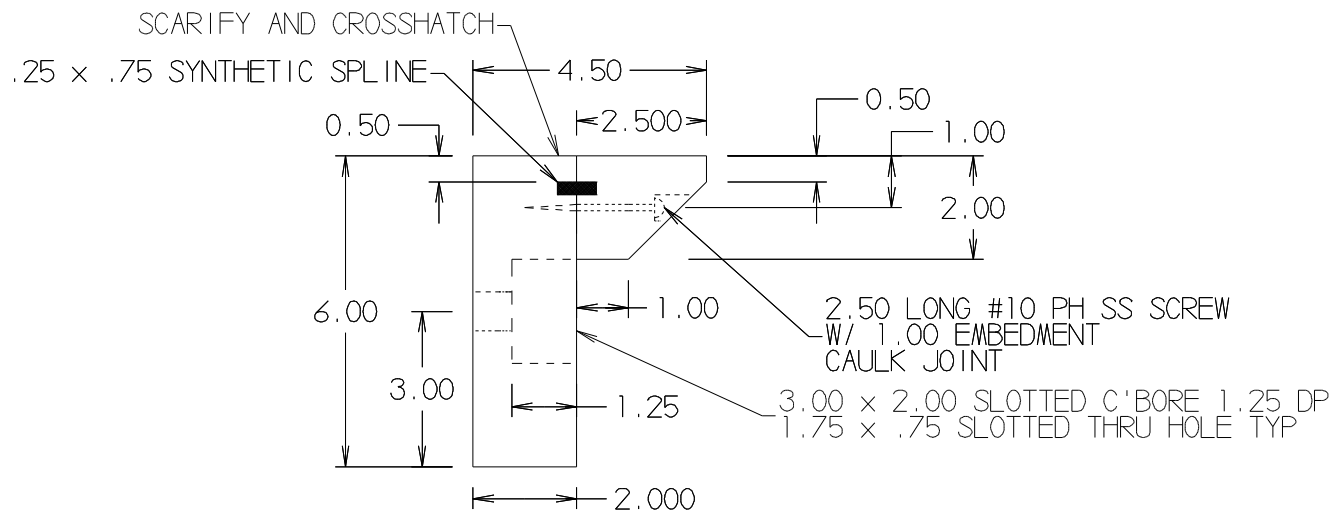

TYP SLOTTED C'BORED HOLE

ADA Boarding Areas at Middletown  
Road and Burnside Ave




|                                              |     |   |                          |
|----------------------------------------------|-----|---|--------------------------|
| UNLESS OTHERWISE SPECIFIED<br>UNITS = INCHES |     | POLYMER INDUSTRIES - ULTRAPOLY DIVISION<br>2404 CENTER STREET - TACOMA, WA - 98409                                                                                              |                          |
| X.X                                          | +/- | .125   |                          |
| X.XX                                         | +/- | .063   |                          |
| X.XXX                                        | +/- | .032   |                          |
| ANGLES                                       | +/- | 1.0°   |                          |
| DRAWN BY<br>BDO                              |     | TITLE<br>4.50 x 6.00 2-PC PROFILE   |                          |
| CHECKED BY<br>BDO                            |     | REF<br>-   | REV<br>-                 |
| DATE<br>03/07/2025                           |     | MATERIAL<br>POLYSLICK AR819FR YELLOW   | DWG NO<br>PU-250307-TS-2 |
| DATE<br>03/07/2025                           |     | POLYMER INDUSTRIES PROPRIETARY, CONFIDENTIAL, AND/OR TRADE SECRET<br>DO NOT USE, REPRODUCE, PUBLISH OR DISCLOSE TO OTHERS WITHOUT EXPRESS WRITTEN AUTHORIZATION BY POLYMER IND. |                          |

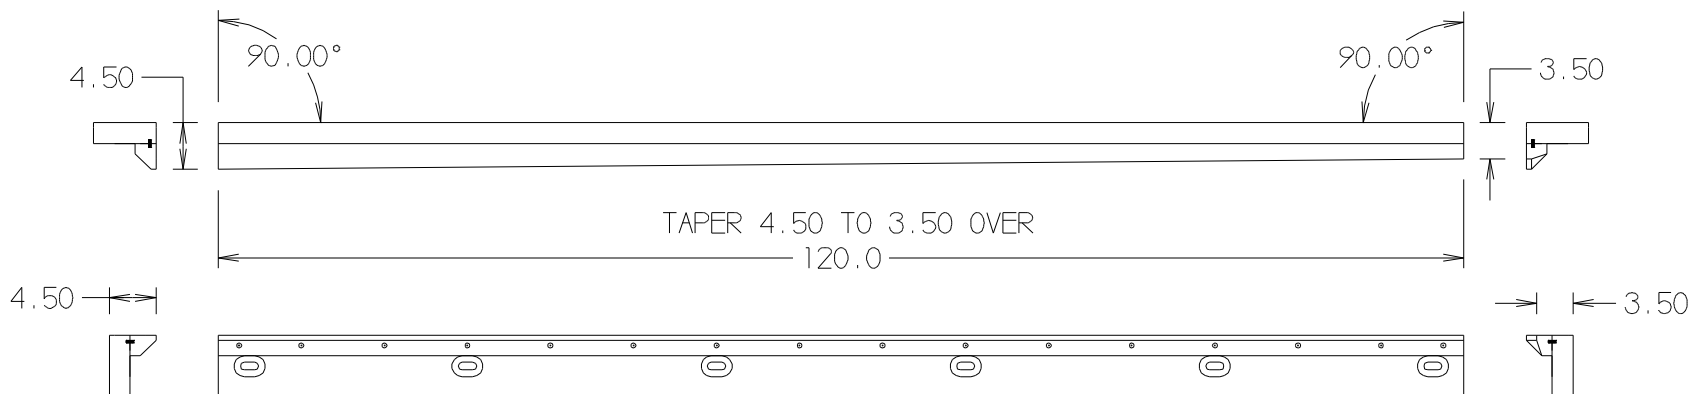

REF PU-250307-TS-1 FOR ALL DETAIL OTHER THAN TAPER

Transition from ADA Boarding Areas  
to Non-ADA Boarding Areas (existing)  
at Middletown Road

|                                                                    |                    |   |                          |
|--------------------------------------------------------------------|--------------------|---|--------------------------|
| UNLESS OTHERWISE SPECIFIED<br>UNITS = INCHES                       |                    | POLYMER INDUSTRIES - ULTRAPOLY DIVISION<br>2404 CENTER STREET - TACOMA, WA - 98409                                                                                              |                          |
| X.X +/- .125<br>X.XX +/- .063<br>X.XXX +/- .032<br>ANGLES +/- 1.0° |                    | TITLE<br>4.50 TO 3.50 X 6.00 2-PC TAPER   |                          |
|                                                                    |                    | REF<br>-   | REV<br>-                 |
| DRAWN BY<br>BDO                                                    | DATE<br>10/20/2025 | MATERIAL<br>POLYSLICK AR819FR YELLOW   | DWG NO<br>PU-251020-TS-1 |
| CHECKED BY<br>BDO                                                  | DATE<br>10/20/2025 | POLYMER INDUSTRIES PROPRIETARY, CONFIDENTIAL, AND/OR TRADE SECRET<br>DO NOT USE, REPRODUCE, PUBLISH OR DISCLOSE TO OTHERS WITHOUT EXPRESS WRITTEN AUTHORIZATION BY POLYMER IND. |                          |

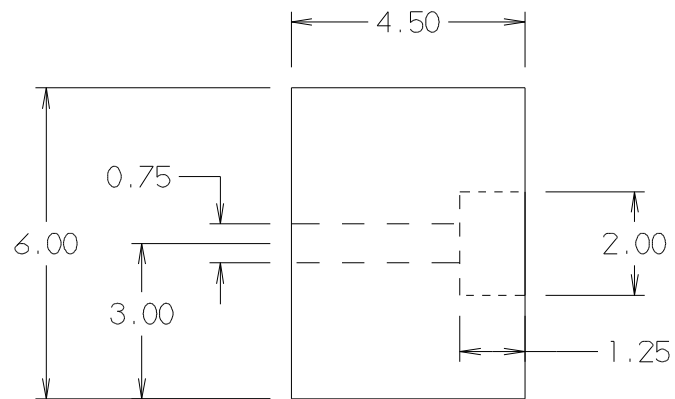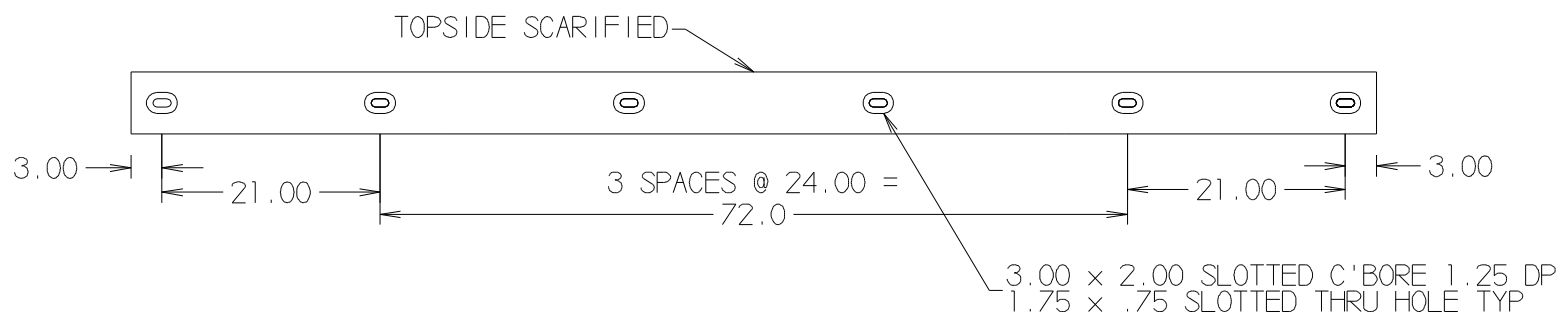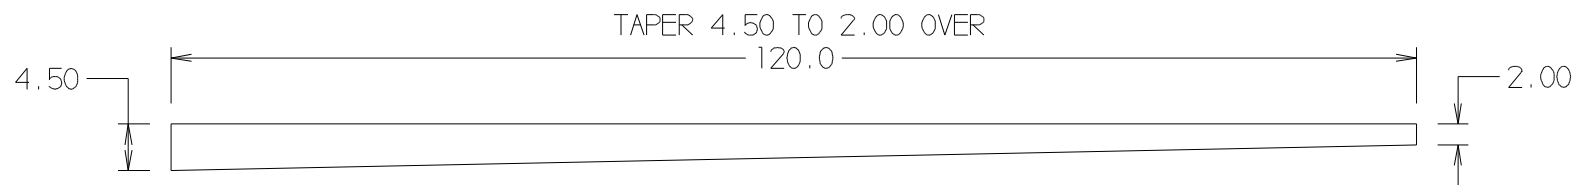

END VIEW  
5:1

**Transition from ADA Boarding Areas  
to End of Platform at Burnside Ave**

|                                                                    |                    |   |                          |
|--------------------------------------------------------------------|--------------------|---|--------------------------|
| UNLESS OTHERWISE SPECIFIED<br>UNITS = INCHES                       |                    | POLYMER INDUSTRIES - ULTRAPOLY DIVISION<br>2404 CENTER STREET - TACOMA, WA - 98409                                                                                              |                          |
| X.X +/- .125<br>X.XX +/- .063<br>X.XXX +/- .032<br>ANGLES +/- 1.0° |                    | TITLE<br>4.5 TO 2 x 6 x 120 1-PC TAPER   |                          |
|                                                                    |                    | REF   | REV<br>—                 |
| DRAWN BY<br>BDO                                                    | DATE<br>10/20/2025 | MATERIAL<br>AR819FR YELLOW   | DWG NO<br>PU-251020-TS-2 |
| CHECKED BY<br>BDO                                                  | DATE<br>10/20/2025 | POLYMER INDUSTRIES PROPRIETARY, CONFIDENTIAL, AND/OR TRADE SECRET<br>DO NOT USE, REPRODUCE, PUBLISH OR DISCLOSE TO OTHERS WITHOUT EXPRESS WRITTEN AUTHORIZATION BY POLYMER IND. |                          |